


LEGEND

AREA WITH MOBILE SERVICES
TOTAL AREA: 875 m²

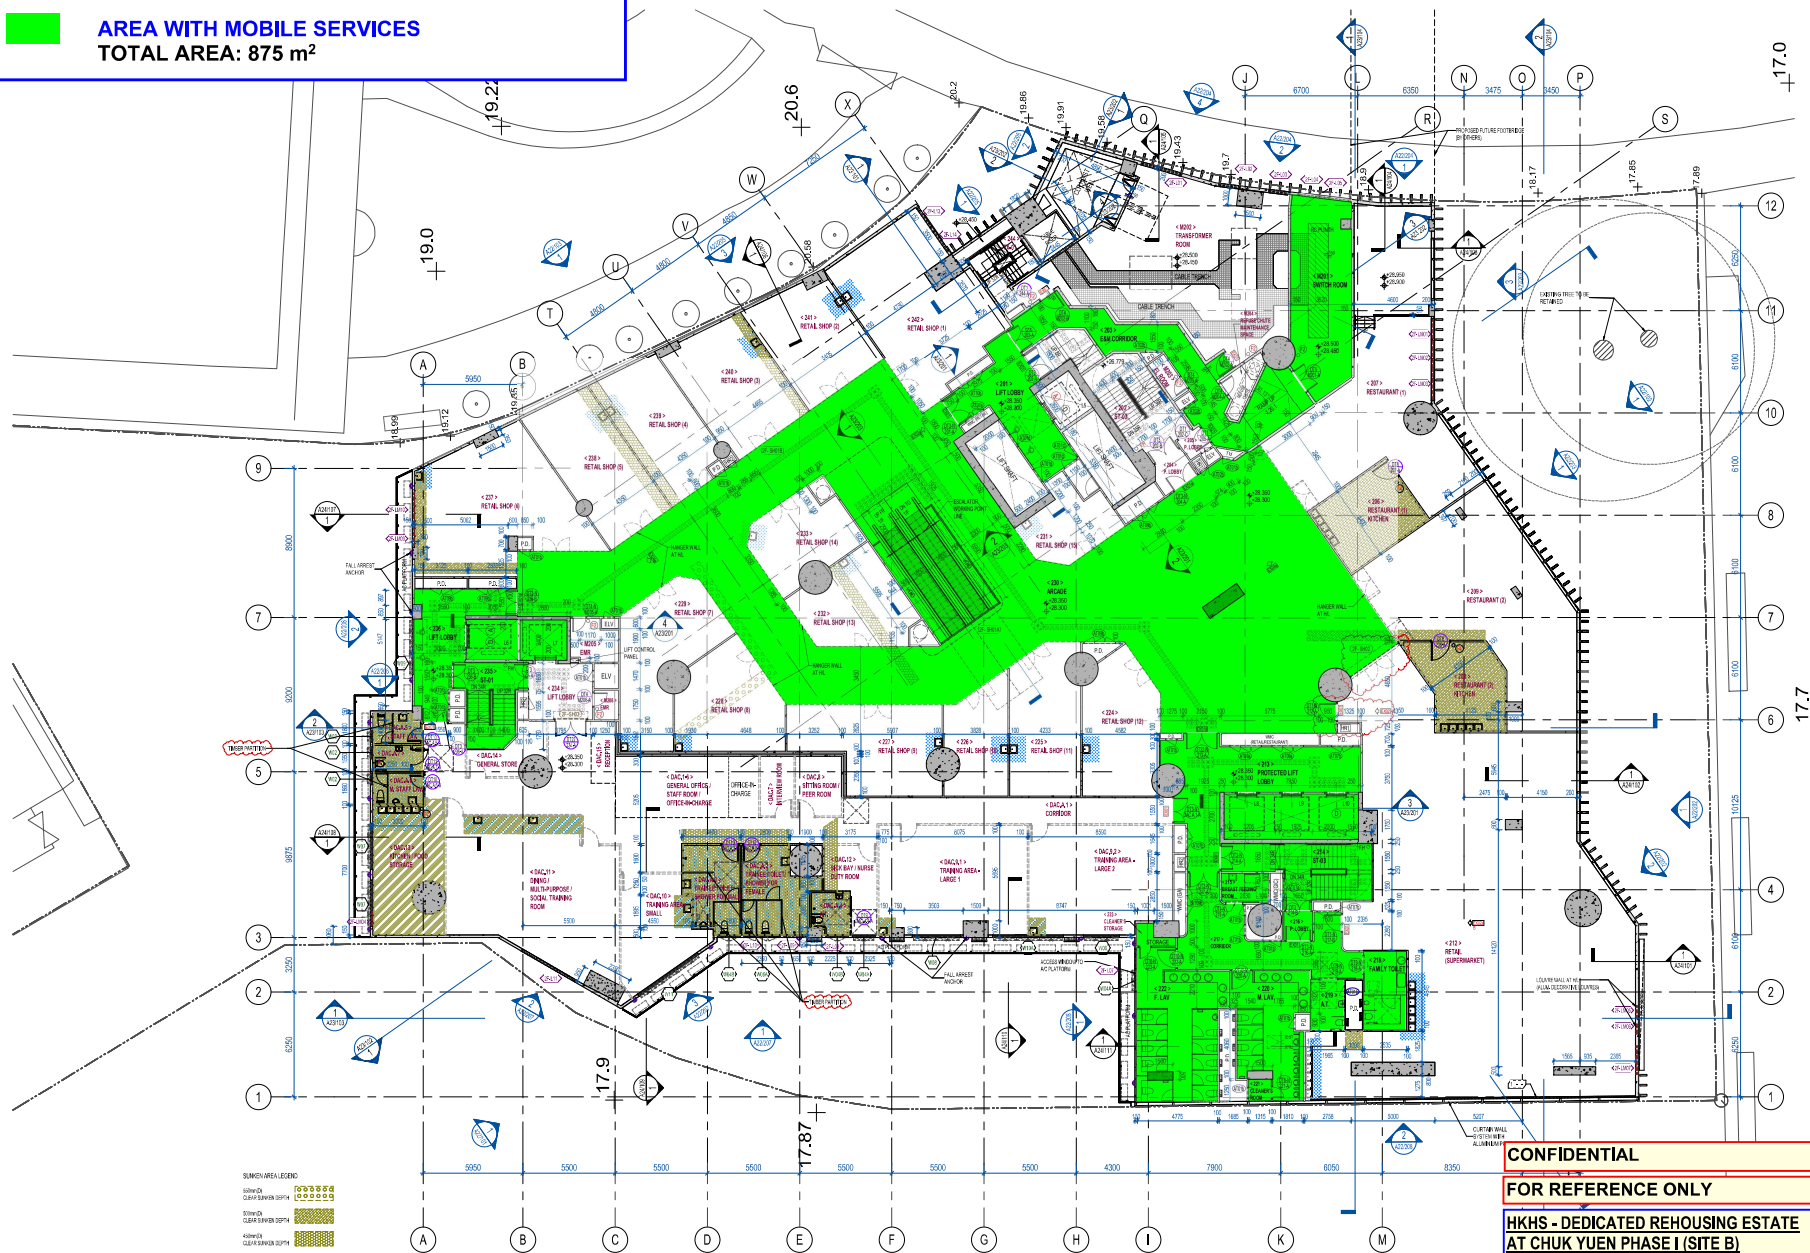

SUNSHEN AREA LEGEND

60mm(2") CLEAR SUNSHEN DEPTH	
50mm(2") CLEAR SUNSHEN DEPTH	
40mm(1 1/2") CLEAR SUNSHEN DEPTH	
40mm(1 1/2") CLEAR SUNSHEN DEPTH	
30mm(1") CLEAR SUNSHEN DEPTH	
30mm(1") CLEAR SUNSHEN DEPTH	
WATERPROOFING MEMBRANE LAYER FOR SAND/RETA. SHOP DECK	

NOTES:
DO NOT SCALE DRAWING, FIGURED DIMENSIONS ARE TO BE FOLLOWED.
READ THIS DRAWING IN CONNECTION WITH GENERAL ARCHITECTURAL PLANS, STRUCTURAL PLANS, AND OTHER RELATED DRAWINGS, THE ARCHITECT SHALL BE NOTIFIED IMMEDIATELY OF ANY DISCREPANCY FOUND THEREIN.
COPYRIGHT OF THIS DRAWING RESERVED BY ARCHITECT.

[illegible]

CLIENT:



WONG TUNG & PARTNERS LIMITED
ARCHITECTS & PLANNERS
18/F, 14 Taikoo Wan Road, Taikoo Shing, Hong Kong
T 852-2803 9888 F 852-2513 1728 www.wongtung.com

PROJECT:
DEDICATED REHOUSING ESTATE AT
CHUK YUEN PHASE I (SITE B)
WONG TAI SIN NKIL LOT NO.6660

TITLE:
GENERAL SETTING OUT AND
ARRANGEMENT PLAN - 2ND FLOOR

CONFIDENTIAL

FOR REFERENCE ONLY

**HKHS - DEDICATED REHOUSING ESTATE
AT CHUK YUEN PHASE I (SITE B)**

TITLE: 2ND FLOOR LAYOUT PLAN
(SHEET 5 OF 7)
DWG. NO.: 2504423A-SK/GN-006
SCALE: 1:150 @A1
DATE: 31 MARCH 2026

DATE: 07/25		SCALE: As indicated	
DRAFTED: (WHK)	CHECKED: (EXL)	DESIGNED: (THG)	REVIEWED: (LP)
JOB NO.	DRAWING NO.		REV. NO.
J032900	T/A21/105		4