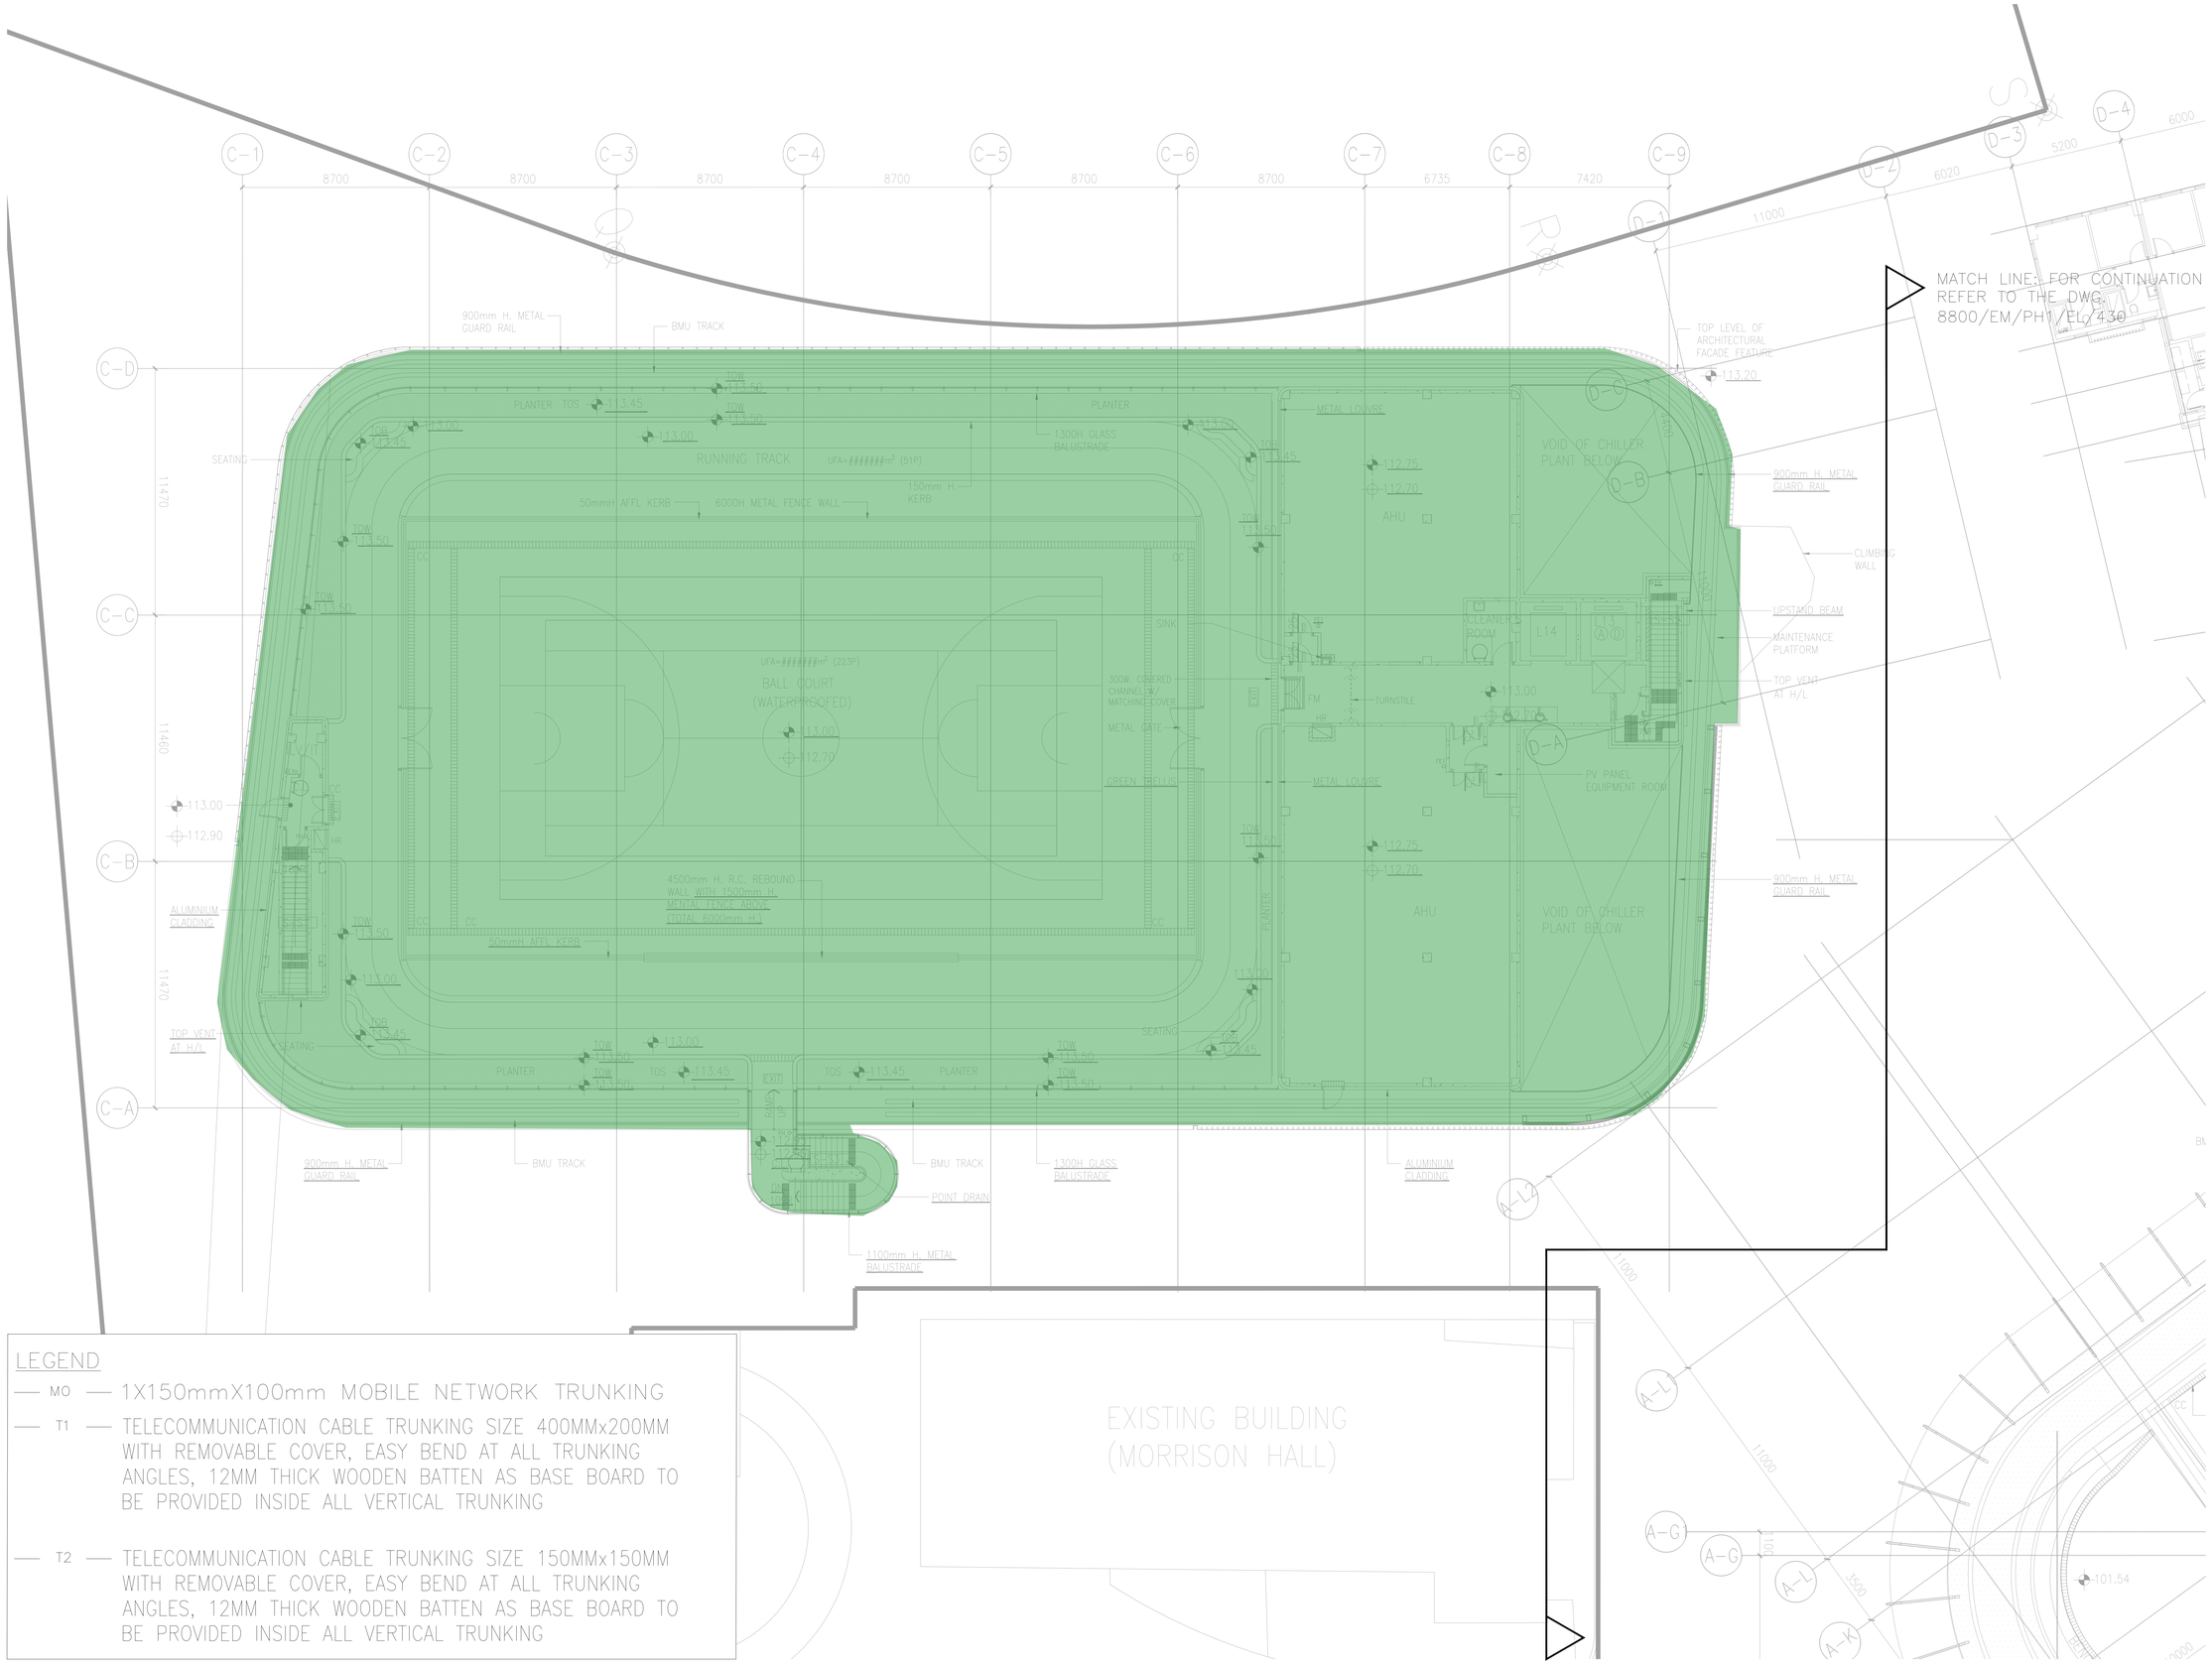


LEGEND

— MO — 1X150mmX100mm MOBILE NETWORK TRUNKING

— T1 — TELECOMMUNICATION CABLE TRUNKING SIZE 400MMx200MM WITH REMOVABLE COVER, EASY BEND AT ALL TRUNKING ANGLES, 12MM THICK WOODEN BATTEN AS BASE BOARD TO BE PROVIDED INSIDE ALL VERTICAL TRUNKING

— T2 — TELECOMMUNICATION CABLE TRUNKING SIZE 150MMx150MM WITH REMOVABLE COVER, EASY BEND AT ALL TRUNKING ANGLES, 12MM THICK WOODEN BATTEN AS BASE BOARD TO BE PROVIDED INSIDE ALL VERTICAL TRUNKING

NOTES:

CONSTRUCTION DRAWING

C.I. NO. : JV-BS-031

REV	DATE	DESCRIPTION
C	03/2026	CONSTRUCTION DRAWING
B	12/2025	CONSTRUCTION DRAWING
A	06/2023	CONSTRUCTION DRAWING

THE OWNERSHIP OF THE COPYRIGHT OF THIS DRAWING IS RETAINED BY J. ROGER PRESTON LTD., WHOSE CONSENT MUST BE OBTAINED BEFORE ANY USE OR REPRODUCTION OF THE DRAWING OR ANY PART THEREOF CAN BE MADE ©20

J. ROGER PRESTON LIMITED
遵信工程顧問有限公司
MECHANICAL AND ELECTRICAL CONSULTING ENGINEERS

PROJECT :

PROPOSED CAPITAL DEVELOPMENT COMPLEX AT THE POKIFIELD ROAD SITE

CLIENT :

THE UNIVERSITY OF HONG KONG

ARCHITECT :

P & T ARCHITECTS AND ENGINEERS LTD

DRAWING TITLE :

HIGH LEVEL CABLE CONTAINMENT LAYOUT FOR PHASE 1 R/F (1 OF 3)

DRAWING NUMBER	REV.
8800/EM/PH1/EL/429	C

SCALE	PRINT DATE
1:100@A0	03/2026
DESIGNED BY	CHECKED BY
AC	TC
DRAWN BY	APPROVED BY
QF	JL