


NOTES:
DO NOT SCALE DRAWING, FIGURED DIMENSIONS
ARE TO BE FOLLOWED.
READ THIS DRAWING IN CONNECTION WITH GENERAL
ARCHITECTURAL PLANS, STRUCTURAL PLANS,
AND OTHER RELATED DRAWINGS. THE ARCHITECT
SHALL BE NOTIFIED IMMEDIATELY OF ANY
DISCREPANCY FOUND THEREIN.
COPYRIGHT OF THIS DRAWING RESERVED BY
ARCHITECT.

ARCHITECTURAL PLANS, STRUCTURAL PLANS, ARCHITECTURAL PLANS, STRUCTURAL PLANS, ARCHITECT AND OTHER RELATED DRAWINGS, THE ARCHITECT SHALL BE NOTIFIED IMMEDIATELY OF ANY DISCREPANCY FOUND THEREIN. COPYRIGHT OF THIS DRAWING RESERVED BY ARCHITECT.

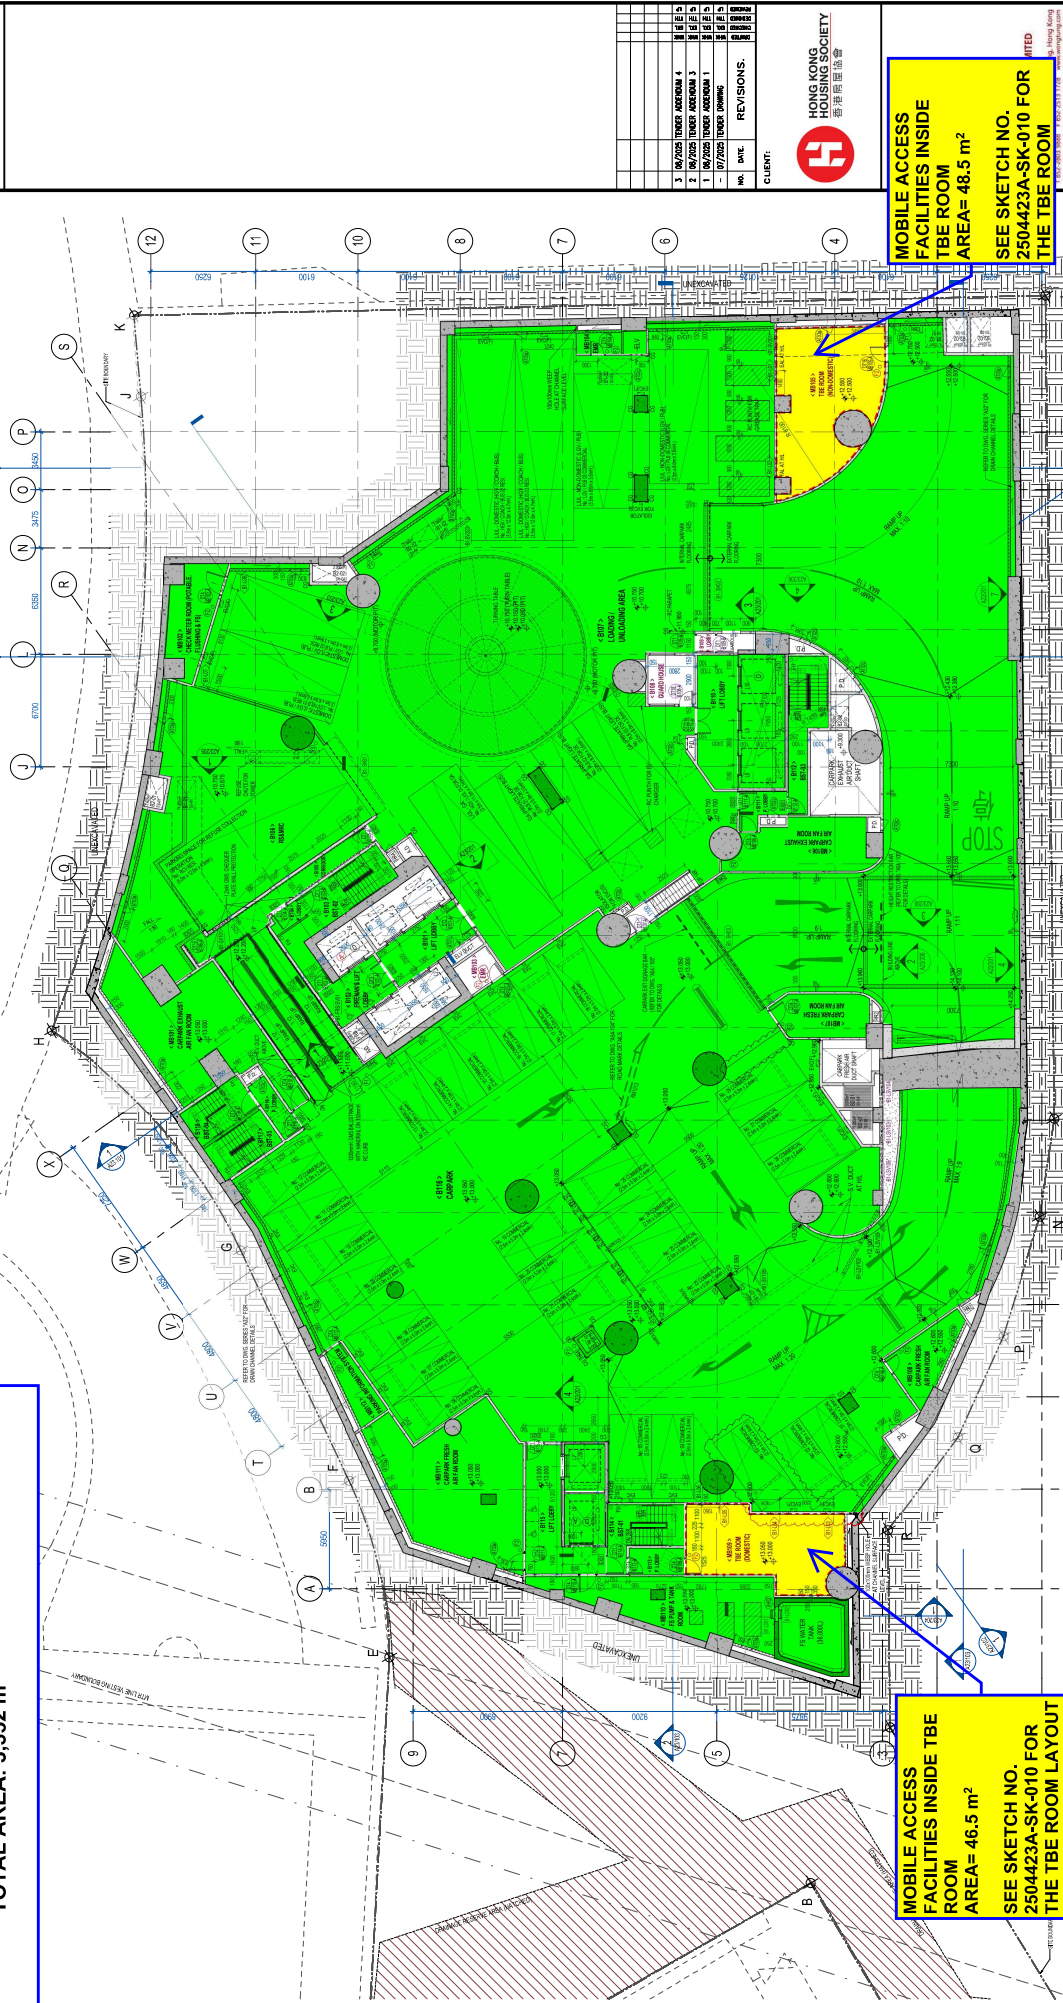

**MOBILE ACCESS
FACILITIES INSIDE
TBE ROOM
AREA= 48.5 m²
SEE SKETCH NO.
2504423A-SK-010 FOR
THE TBE ROOM**

SEE SKETCH NO.

THE TBE ROOM

**DEDICATED REHOUSING ESTATE AT
CHUIK YUEN PHASE I (SITE B)**

WONG TAI SIN NKIL LOT NO.6660

TITLE:
GENERAL SETTING OUT AND

1000

DATE:	07/25	SCALE:	1 : 150
DRAFTED:	CHECKED:	DESIGNED:	REVIEWED:

(MMK)	(EXC.)	(TIN)	(L.P.)
JOB NO.	ORDERING NO.		REV. NO.

J032900	T/A21/102	3
---------	-----------	---

J032900	I/A21/102	3
---------	-----------	---
