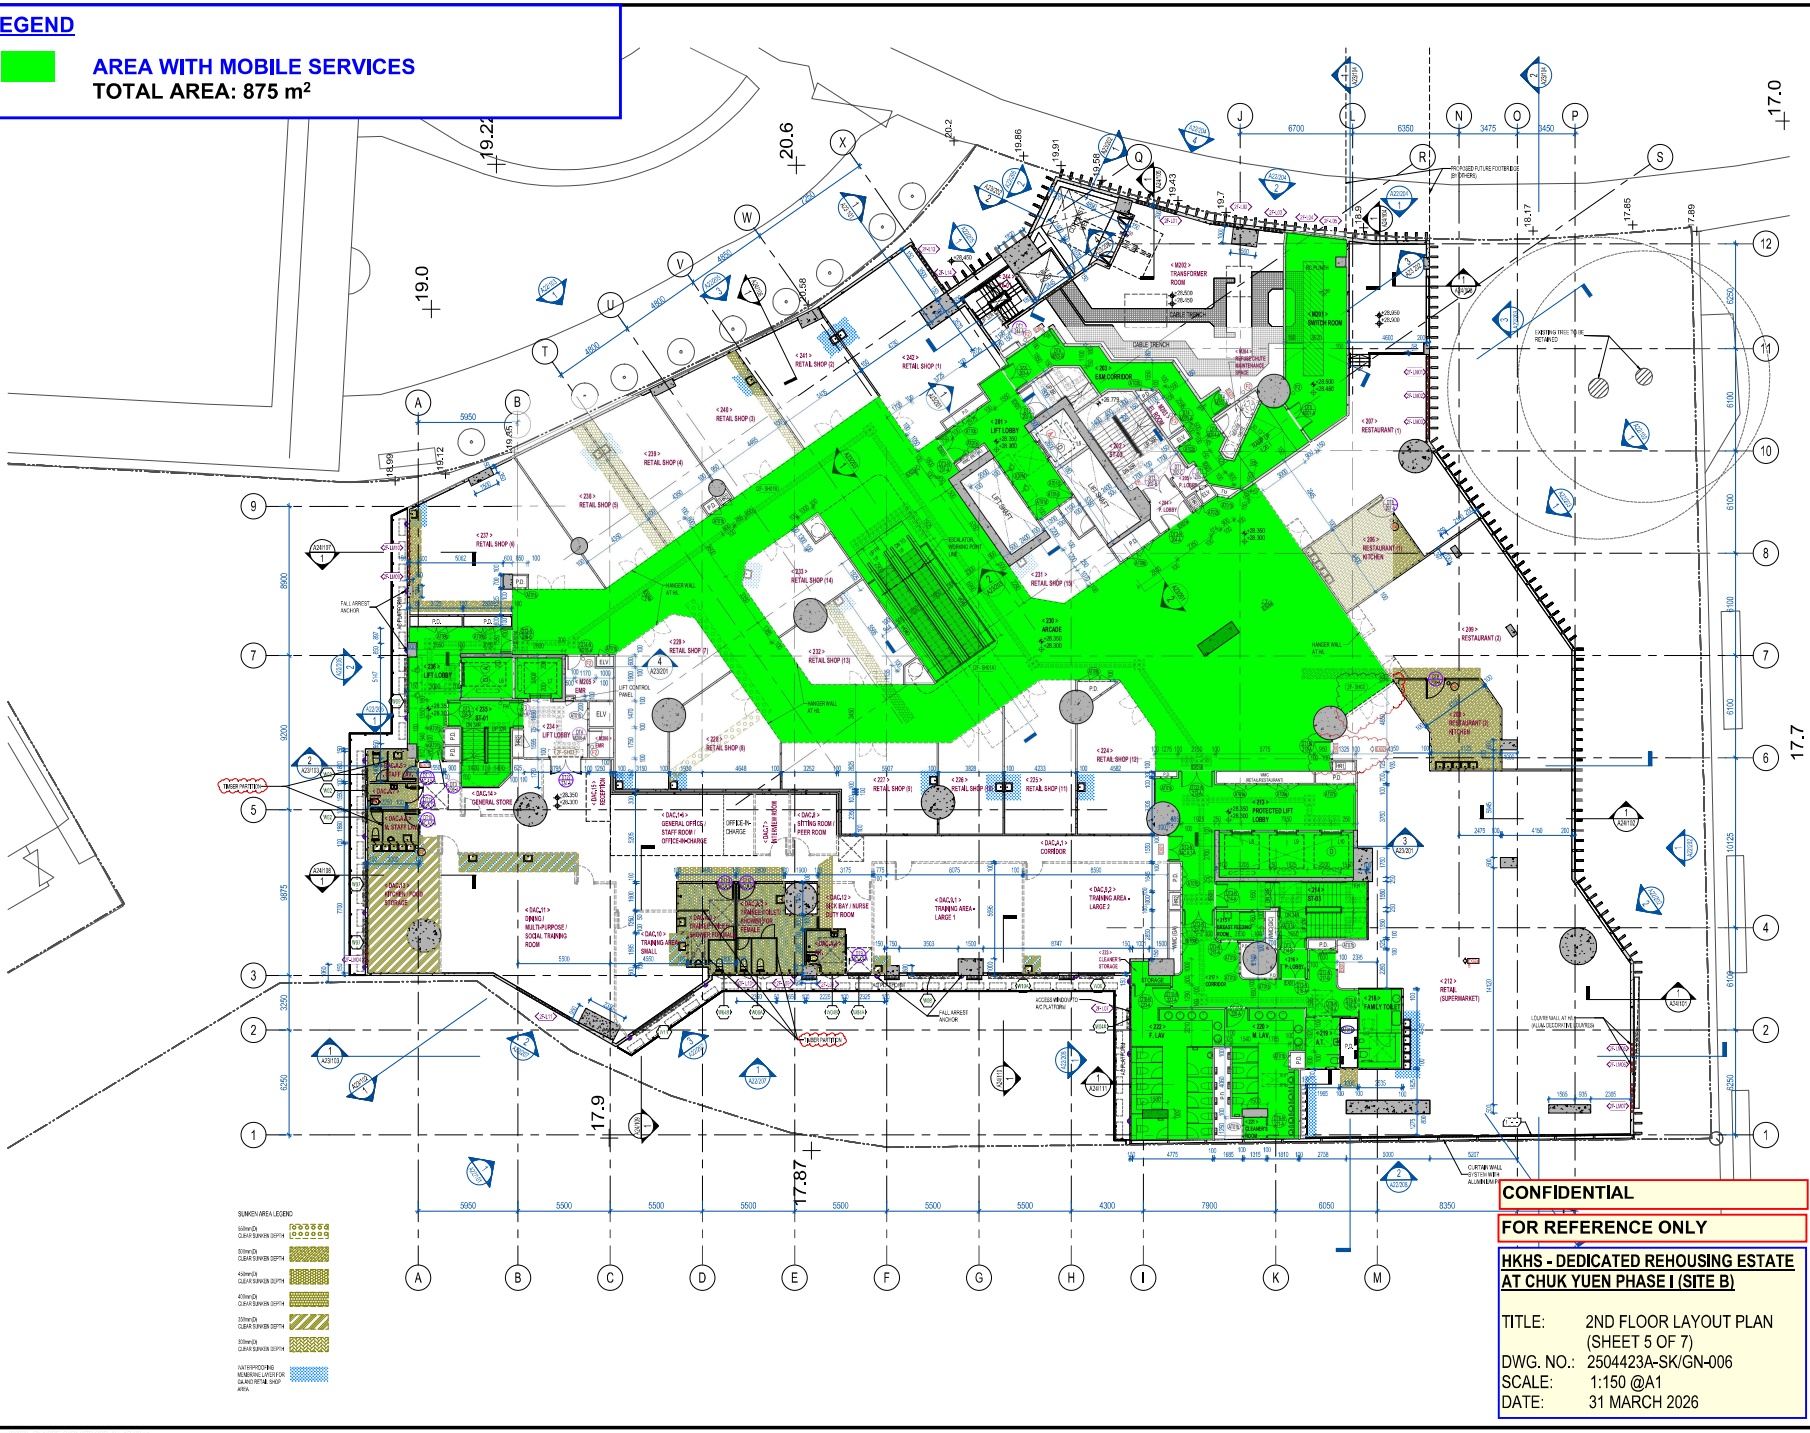

NOTES:
DO NOT SCALE DRAWING, FIGURED DIMENSIONSNT ARE TO BE FOLLOWED.
READ THIS DRAWING IN CONNECTION WITH GENERAL ARCHITECTURAL PLANS, STRUCTURAL PLANS, AND OTHER RELATED DRAWINGS, THE ARCHITECT SHALL BE NOTIFIED IMMEDIATELY OF ANY DISCREPANCY FOUND THEREIN.
COPYRIGHT OF THIS DRAWING RESERVED BY ARCHITECT.

NO.	DATE.	REVISIONS.	DRAWN	CHECKED	DESIGNED	APPROVED
4	09/2025	TENDER ADDENDUM 5	MK	MK	EL	TP
3	08/2025	TENDER ADDENDUM 4	MK	MK	EL	TP
2	08/2025	TENDER ADDENDUM 3	MK	MK	EL	TP
1	08/2025	TENDER ADDENDUM 1	EL	EL	TP	TP
-	07/2025	TENDER DRAWING	MK	MK	EL	TP

CLIENT:
HONG KONG HOUSING SOCIETY
香港房屋協會

WONG TUNG & PARTNERS LIMITED
ARCHITECTS & PLANNERS
18/F, 14 Taikoo Wan Road, Taikoo Shing, Hong Kong
T 852-2803 9888 F 852-2513 1728 www.wongtung.com

PROJECT:
DEDICATED REHOUSING ESTATE AT CHUK YUEN PHASE I (SITE B)
WONG TAI SIN NKIL LOT NO.6660

TITLE:
GENERAL SETTING OUT AND ARRANGEMENT PLAN – 2ND FLOOR

DATE:	07/25	SCALE:	As indicated
DRAWN: (MK)	CHECKED: (EKL)	DESIGNED: (TP/H)	REVIEWED: (LP)
JOB NO.	DRAWING NO.		REV. NO.
J032900	T/A21/105		4

CONFIDENTIAL

FOR REFERENCE ONLY

HKHS - DEDICATED REHOUSING ESTATE AT CHUK YUEN PHASE I (SITE B)

TITLE: 2ND FLOOR LAYOUT PLAN (SHEET 5 OF 7)
DWG. NO.: 2504423A-SK/GN-006
SCALE: 1:150 @A1
DATE: 31 MARCH 2026